


BOUTIQUE APARTMAN RIPENDA

PRILOZI — TLOCRT, INSTALACIJE I FASADE — FINALNA VERZIJA R8

Projekt	Boutique Apartman Ripenda
Investitor	Sandra Antunović
Lokacija	Ripenda, Labin
Mjerilo	1:50 (detalji 1:10)
Revizija	R8 — anteroom uklonjen, kupaonica proširena (3,94×1,60m), bedroom smanjena (3,94×2,76m), pregrada CW100 (12,5cm), P1 premješten na stražnji zid, fasade gespiegelt, kanalizacija uz središnji zid (zalivena u estrihu), stolarija i kanalizacija ažurirane 31.08.2026.
Datum	26.08.2026. Korekcije: 31.08.2026.

Ovaj dokument objedinjuje tekstualno-tablični opis tlocrta, instalacija i fasada. Grafički CAD/vektorski prilozi (SVG crteži) čuvaju se odvojeno kao radna podloga; ovdje su konsolidirane sve kote, oznake i opisi u finalnom, usklađenom obliku.

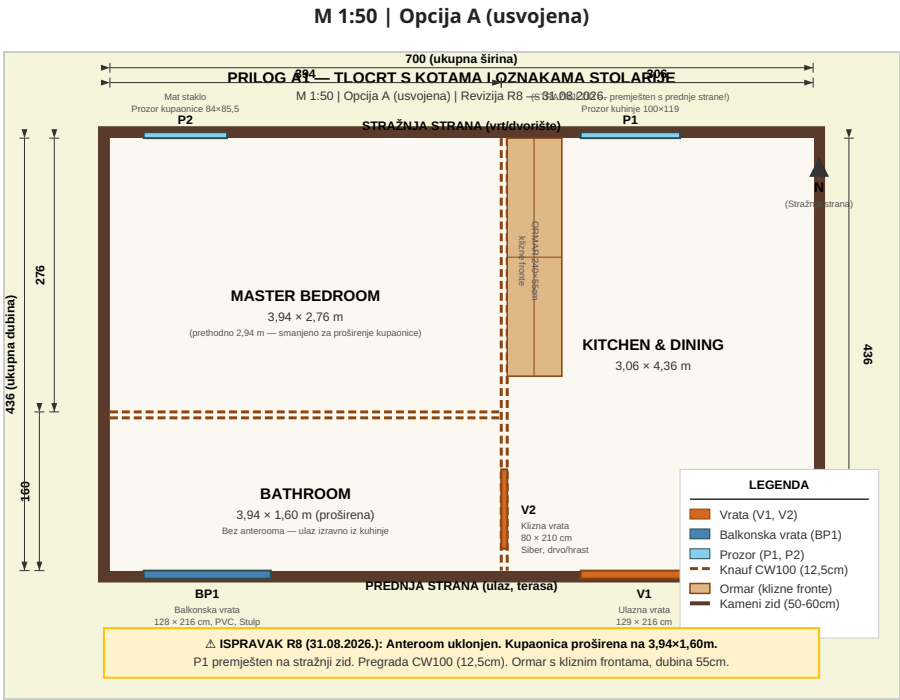

Raspored prostorija (Opcija A — usvojena)

Prostorija	Dimenzije	Položaj u kući
Master Bedroom	3,94×2,76 m	Prednji lijevi dio (uz terasu/ulaz)
Kitchen & Dining	3,06×4,36 m	Desni dio, puna dubina kuće
Bathroom (proširena)	3,94×1,60 m	Stražnji lijevi dio, puna širina — ulaz izravno iz kuhinje

Ispravak 31.08.2026. (R8): Hodnik (anteroom) je u cijelosti uklonjen iz tlocrta; kupaonica se proširila preko tog prostora. Pregrada između sobe i kupaonice je Knauf CW100/UW100 (ukupna debljina 12,5 cm). Ukupne vanjske gabarite kuće: 7,00 m (širina) × 4,36 m (dubina). Sjever prema tlocrtu — orijentacija prednje strane prema ulici/ulazu, stražnje prema dvorištu. Debljina kamenih bočnih zidova: 500–600 mm (okvirna procjena — provjeriti na licu mjesta).

Tablica oznaka stolarije — FINALNO R8

Oznaka	Naziv	Dimenzije	Napomena
V1	Ulazna vrata	129 cm ukupno (93+36 fiksni)	Mat staklo na fiksnom dijelu, obostrana kvaka; ažurirano 31.08.2026.
V2	Klizna vrata kupaonice	80×210 cm	Šiber sustav; ulaz izravno iz kuhinje
P1	Prozor kuhinje	100×119 cm	Vanjska ALU grilja RAL 7016 — grilje treba uskladiti s novom mjerom; POZICIJA: stražnji zid ; ažurirano 31.08.2026.
P2	Prozor kupaonice	84×85,5 cm	Matirano staklo; ažurirano 31.08.2026.
BP1	Balkonska vrata (spavaća soba)	128×216 cm	PVC, Stulp, s griljama RAL 7016 — mjera prema revidiranoj ponudi Eko4u (31.08.2026.); grilje treba uskladiti s novom mjerom

Ormar (Master Bedroom)

Element	Specifikacija
Pozicija	Uz Knauf pregradu, u spavaćoj sobi
Dimenzije	270×240×55 cm (V×Š×Dub)
Fronte	Klizne (šiber sustav) — ne push-open
Boja	Hrast
Razlog kliznih fronti	Prolaz pored kreveta je samo 76 cm širok; klizne fronte ne zauzimaju dodatni prostor pri otvaranju

Prolazni koridor pored kreveta


Širina prostora između kreveta (180 cm) i Knauf pregrade (12,5 cm) s ormarom (55 cm):

$394\text{ cm (ukupna širina sobe)} - 180\text{ cm (krevet)} - 12,5\text{ cm (pregrada)} - 55\text{ cm (ormar)} - 70\text{ cm (rezerva)} = 76,5\text{ cm slobodnog prolaza}$

Ovo je minimalna, ali funkcionalna širina prolaza (standard za pristup krevetu je 60–70 cm).

Pregrada CW100 — utjecaj na površine

Prostorija	Neto dimenzije	Površina
Master Bedroom	3,94 × 2,76 m	10,87 m²
Kitchen & Dining	3,06 × 4,36 m	13,34 m²
Bathroom	3,94 × 1,60 m	6,30 m²
UKUPNO NETO		30,51 m² ≈ 30,5 m²

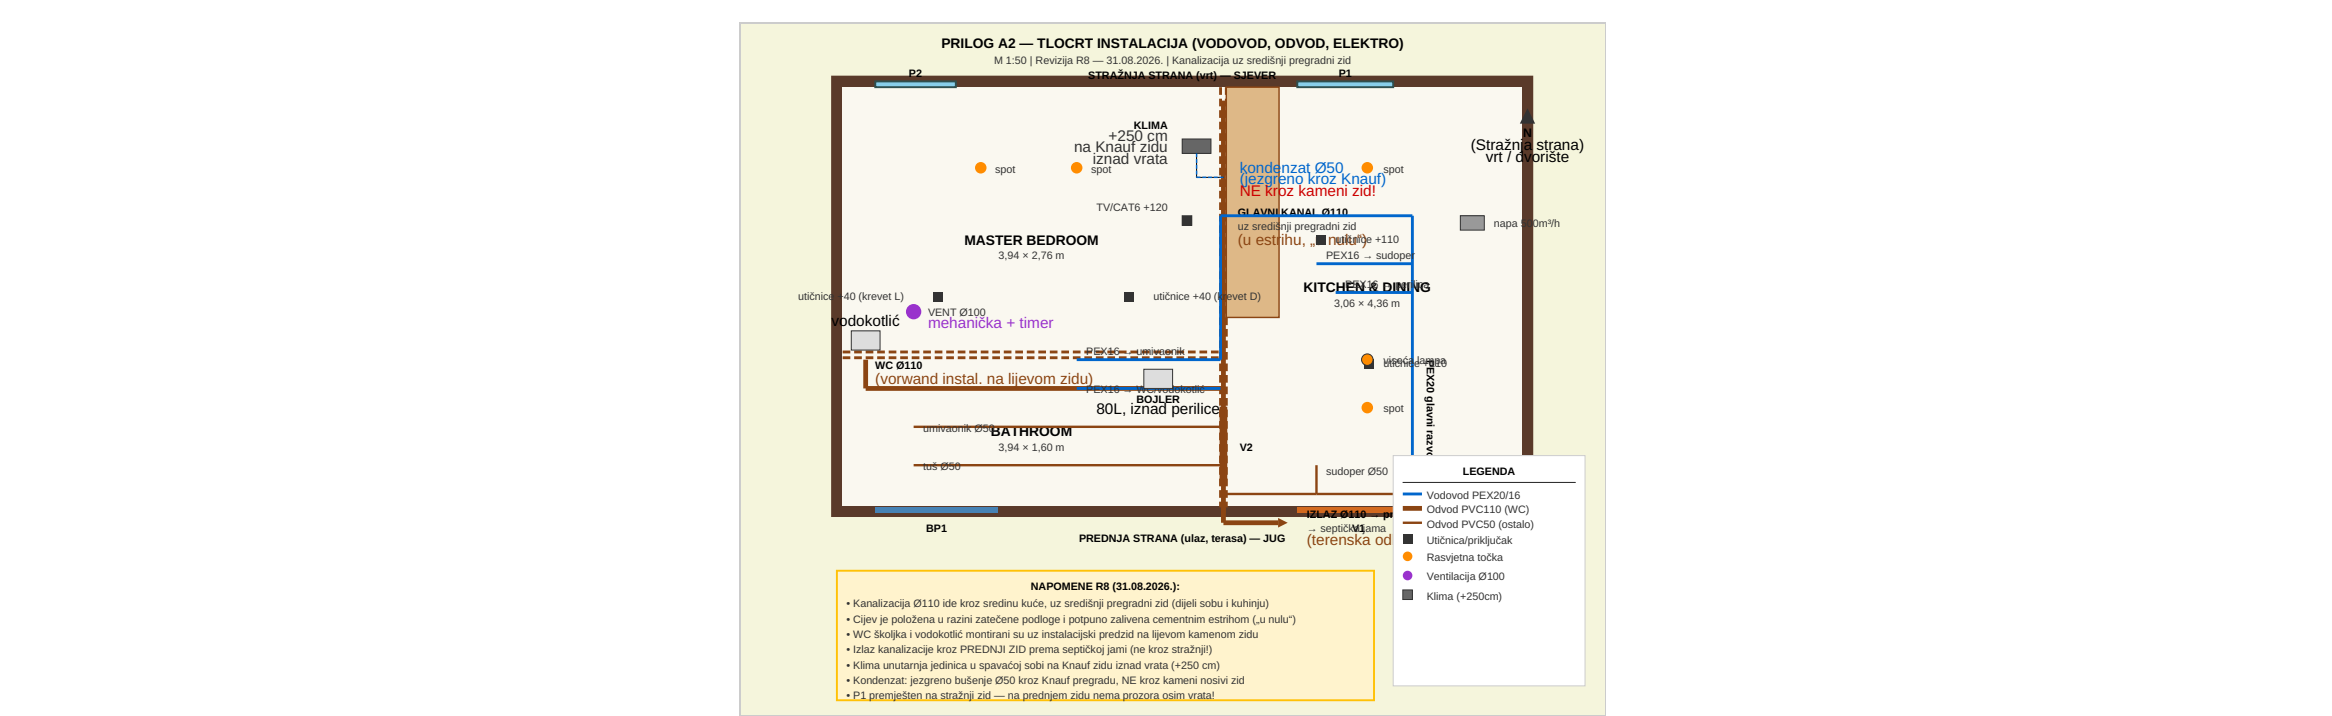

- Glavni kanalizacijski kanal PVC Ø110 vodi se kroz sredinu kuće, uz središnji pregradni zid koji dijeli spavaću sobu i kuhinju. Cijev se polaže u razini zatečene podloge i potpuno se zalijeva cementnim estrihom prilikom niveliranja cijele etaže u jednu ravninu („u nulu“).
- Kod pregrade kupaonice cijev se spaja s WC školjkom i ugradbenim vodikotlicem (koji su montirani uz instalacijski predzid na lijevom kamenom zidu).
- Glavni sabirni kanal vodi se duž tog središnjeg zida ravno prema naprijed i ima konačan izlaz kroz vanjski PREDNJI ZID (strana ulaza/terase); terenska odluka (potvrđeno 31.08.2026.) — direktan spoj na septičku jamu preko vanjskog prostora ispred kuće (alternativa: spoj na postojeću vertikalu "majčin WC" kod kotlovnice, ako se na terenu pokaže povoljnije).
- Dovod hladne/tople vode: PEX 20 mm glavni razvod, PEX 16 mm ogranci (WC/umivaonik/perilica, sudoper).
- Prije zatvaranja poda: donji dio zidova obložiti hidroizolacijskom folijom radi zaštite od vlage.

Legenda vodovod / odvod

Oznaka	Značenje
	Vodovod (dovod) — PEX20 glavni razvod, PEX16 ogranci
	Odvod — PVC110 (WC/gl. kanal), PVC50 (umivaonik/perilica/sudoper)

Legenda elektro


Oznaka	Značenje
	Utičnica/priključak (uz navedenu visinu u cm)
	Rasvjetna točka / viseća lampa
	Ventilacija Ø100
IP44	Zaštićena izvedba (kupaonica)

Mikro-lokacije elektro — ažurirano R8

Uređaj	Visina	Napomena
Klima (unutarnja jedinica)	+250 cm	Spavaća soba, Knauf pregradni zid iznad vrata
TV / Internet (RJ45)	+120 cm	Pregradni Knauf zid u sobi
Utičnice uz krevet	+40 cm	Lijevi i desni bok kreveta
Radne plohe kuhinja	+110 cm	Trostruki blok
LED traka ispod police	+150 cm	Ispod hrastovih polica
Perilica posuđa / rublja	+45 cm	
Napa	—	500 m³/h protočnost
Ventilacija kupaonica	strop (Ø100)	IP44 zaštita; lijevi vanjski zid ili pregradni zid

Napomene instalacija R8

- **Kanalizacija Ø110 ide uz središnji pregradni zid (ne uz vanjsku stijenu), zalivena u estrihu „u nulu“.**
- WC priključak preko vorwand instalacije na lijevom kamenom zidu.
- Svi padovi odvoda min. 2%.
- Vodovodne cijevi izolirati u estrihu.
- Kondenzat klime: jezgreno bušenje Ø50 kroz Knauf pregradu, NE kroz kameni zid.
- Provjeriti sve mjere i kote na licu mjesta.

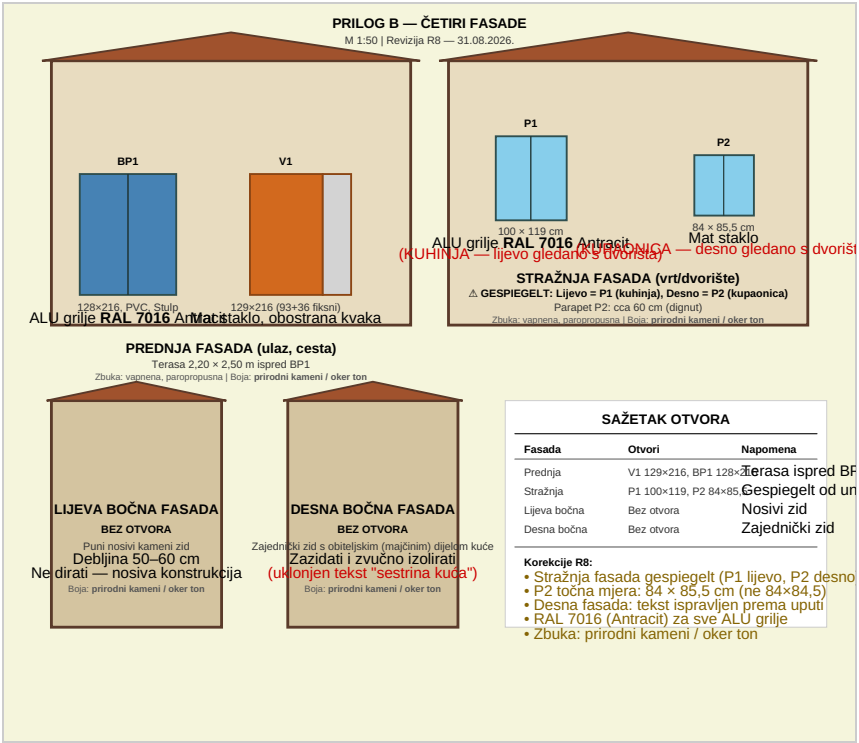


Sažetak otvora po fasadama — R8

Fasada	Otvori	Napomena
Prednja (ulaz, cesta)	Ulazna vrata 129×216, Balkonska vrata 128×216 (PVC/ALU, grilje RAL 7016)	Terasa 2,20×2,50 m ispred balkonskih vrata
Stražnja (vrt/dvorište)	Prozor kuhinje P1 100×119 (LIJEVO), prozor kupaonice P2 84×85,5 (DESNO)	GESPIEGELT — oba otvora zadržana iz postojećeg stanja; P2 parapet cca 60 cm
Lijeva bočna	Bez otvora	Nosivi kameni zid, ne dirati
Desna bočna	Bez otvora	Zajednički zid s obiteljskim (majčinim) dijelom kuće — zazidati i zvučno izolirati

Ključna ispravka R8 — Stražnja fasada: Gledano s dvorišta (vanjske strane), stražnja fasada je gespiegelt u odnosu na unutarnji raspored. U kući je kuhinja desno i kupaonica lijevo, ali gledano s vanjske strane (s dvorišta), prozor kuhinje (P1, veći) je lijevo, a prozor kupaonice (P2, manji) je desno. Ovo je standardna arhitektonska konvencija za fasadne crteže. Boja zbuke: prirodni kameni / oker ton. Boja ALU grilja: RAL 7016 Antracit.

M 1:50 | NE AŽURIRANO s izmjenama R8 — povijesna referenca

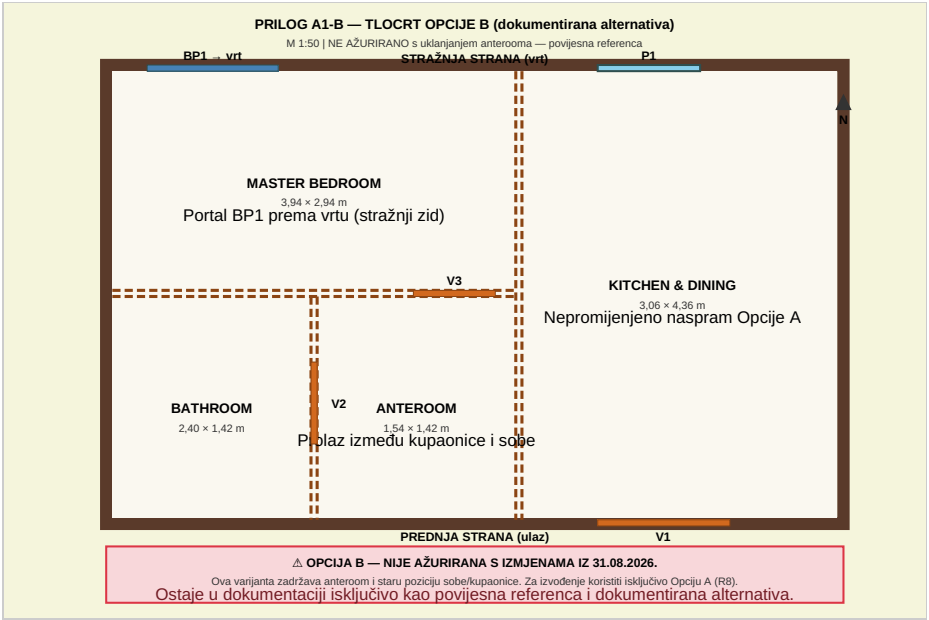

Instalacija	Opcija A (R8)	Opcija B (stara verzija)
Kanalizacija	Jedna grana (kupaonica blizu kuhinje), izlaz kroz prednji zid	Dvije grane → zajednički šaht kod novijeg dijela kuće
Topla voda	Jedan zajednički bojler	Bojler kupaonice + mali protočni bojler 5 L (kuhinja)
Portal/pogled	Prednja strana (terasa, ulica)	Stražnja strana (vrt/dvorište)
Anteroom	Uklonjen (R8)	Zadržan (1,54×1,42 m)

PRILOG A3 — PRESJEK A-A

M 1:50 | Pogled kroz kuhinju i spavaću sobu




#	Sloj / element	Napomena
1	Gotovi pod (mikrocement / alternativa keramika, vidi Elaborat Pogl. 15)	Vidi Prilog A5 – detalj poda
2	Glavna greda (hrast/crnogorica) — NOVA (zamjena, terenska odluka 26.08.2026.)	Raspon 4,36 m, kraća stranica kuće
3	Rog – zadržan vidljiv	Tradicionalni stil
4	Toplinska izolacija iznad rogova	PIR ili kamena vuna
5	Pokrov	Postojeći crijep, zadržan (lomljeni komadi koriste se kao punjenje poda, ne odvoze se)
6	Kameni nosivi zid	500–600 mm, ne dira se

Visine stropa: Master Bedroom 2,91 m, Kitchen & Dining 2,74 m.

Sudarni lim: na spoju krova s gornjim katom (u vlasništvu Sandre) ugrađuje se sudarni zidni lim radi pravilnog odvoda vode na mjestu spoja dviju krovnih razina — potvrđeno na terenu.


PRILOG A5 — DETALJ PODA (1:10)

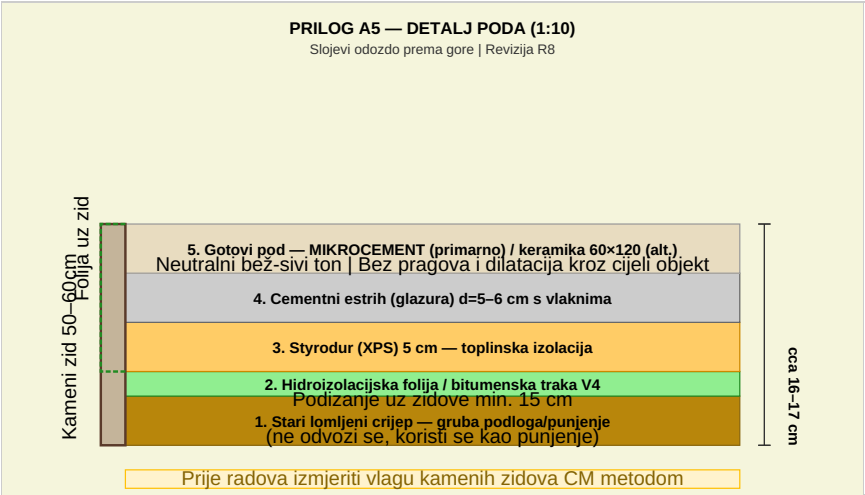

Slojevi (odozdo prema gore): stari lomljeni crijep kao gruba podloga/punjenje → hidroizolacijska folija uz zidove (min. 15 cm) → Styrodur (XPS) 5 cm → cementni estrih s vlaknima → gotovi pod (mikrocement / alternativa keramika).

PRILOG A6 — DETALJ ZIDA KUPAONICE (1:10)

ISPRAVLJENO R8: Pregrada promijenjena s CW75 (10 cm) na CW100 (12,5 cm).

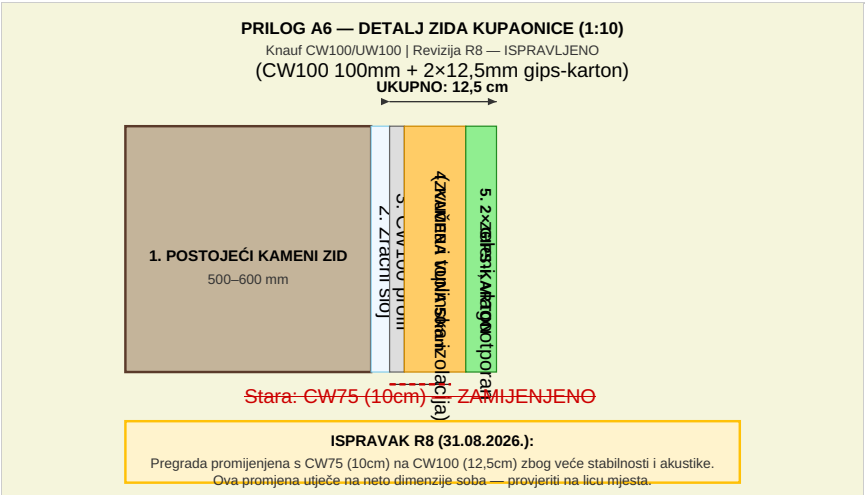

#	Sloj
1	Postojeći kameni zid (500–600 mm)
2	Zračni sloj
3	Knauf CW100 profil
4	Kamena vuna 50 mm
5	Gips-karton (zeleni, vlagootporan), dvostruko — 2×12,5 mm

Ukupna debljina pregrade: 12,5 cm (CW100 100 mm + 2×12,5 mm gips-karton). Ova promjena utječe na neto dimenzije soba — provjeriti na licu mjesta.